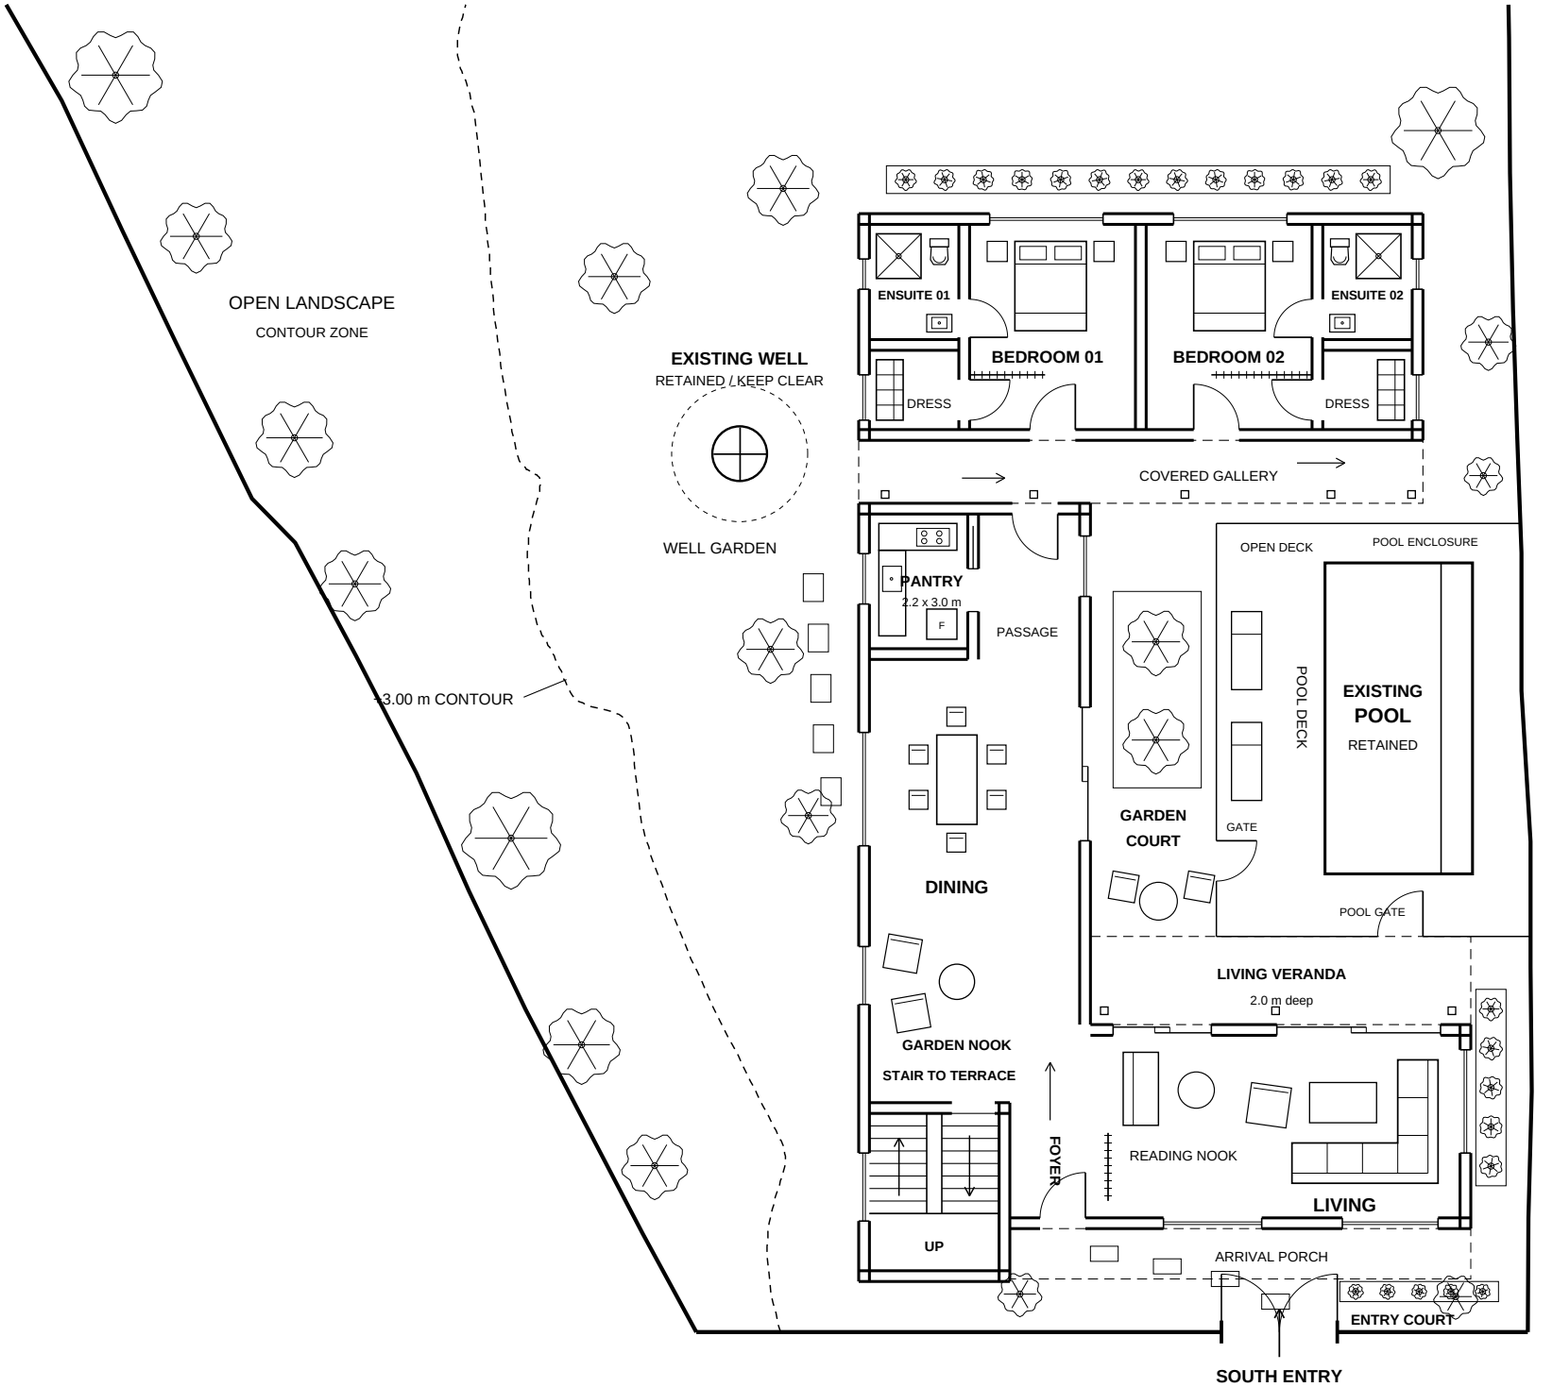

CONCEPT 03

THE GARDEN COURT HOUSE

A sheltered arrival reveals the court.

Living opens to pool and garden.

Sleeping wing remains private.

Screened bedroom vestibules.

One calm family seating group.

Deeper veranda for outdoor living.

APPROX. CLEAR ROOM SIZES

Bedroom 01: 3.7 x 4.6 m

Bedroom 02: 3.7 x 4.6 m

Ensuites: 2.0 x 2.6 m each

Pantry: 2.2 x 3.0 m

Living veranda: 2.0 m deep

Pool deck west: 2.4 m wide

FIXED ELEMENTS RETAINED

Pool, well and +3m contour

traced from the original PDF.

North up / south entry / 240mm walls

Schematic; site levels and setbacks

remain for the next design stage.

0 1 2 5 m

POOMALA

THE GARDEN COURT HOUSE / DEVELOPED CONCEPT 03

A tropical family retreat organised around a planted court · existing pool and well retained

POOMALA

THE GARDEN COURT HOUSE

03 / architectural concept and spatial organisation

SPATIAL ORGANISATION

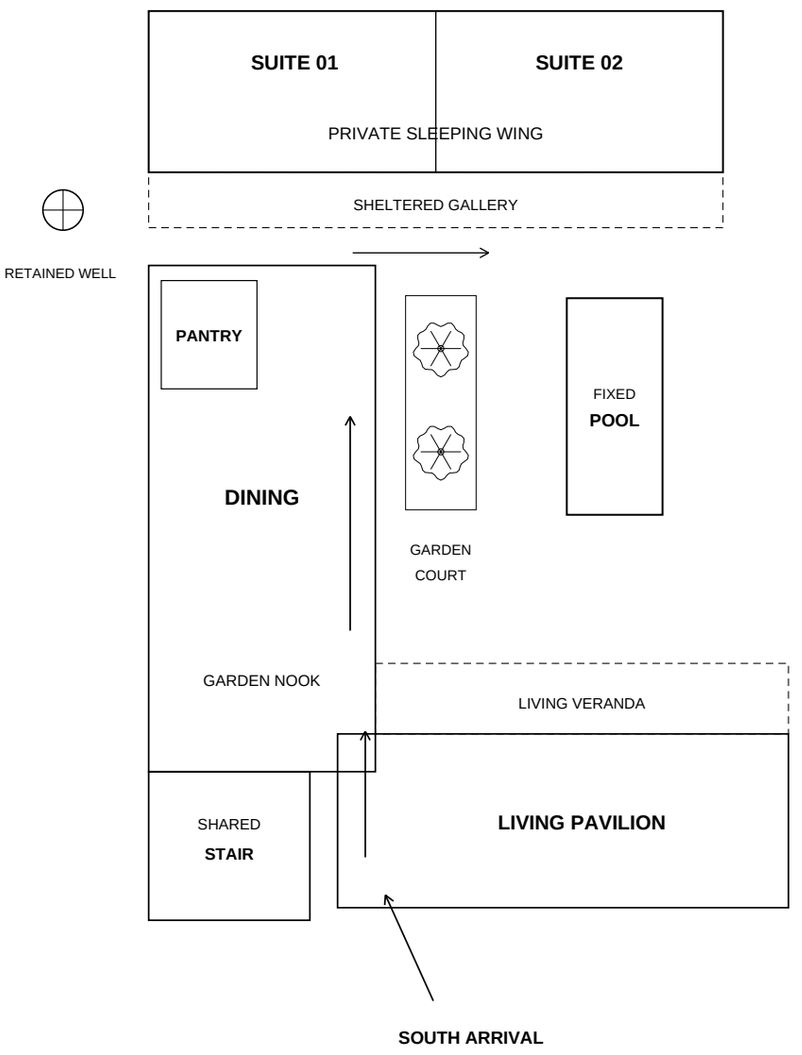

01 / AN ARRIVAL THAT REVEALS THE HOUSE

Gate / garden walk / sheltered porch / screened foyer / court + pool.
The entry screen delays the main view; the court becomes the first reveal.

02 / ONE CENTRE FOR FAMILY LIFE

Living and dining open to the same planted court and pool landscape.
A single family seating group replaces scattered lounge furniture.
The pantry sits beside dining; the terrace stair uses shared circulation.

03 / PRIVACY THROUGH SPACE

The sleeping pavilion is reached through a sheltered gallery.
Screened vestibules conceal the beds from open bedroom doors.
Each suite has a dressing area and its own externally ventilated bathroom.

04 / TROPICAL CHARACTER THROUGH PROPORTION

A deeper living veranda creates a usable outdoor threshold.
Proposed roof hierarchy: a higher living pavilion and quieter bedroom wing.
Light plaster, stone underfoot and timber screens form a restrained palette.

05 / THE EXISTING SITE SETS THE DESIGN

The built pool and well remain in their original positions.
Controlled arrival and gated pool access support family use.
The shown contour stays clear of the new building footprints.

DEVELOPED CONCEPT

Schematic proposal; survey levels, boundaries, structure and statutory setbacks remain to be verified.